


SYMBOL LEGEND

- BC HYDRO
PAD MOUNT TRANSFORMER
- HIGH VOLTAGE OVERHEAD / UNDERGROUND
- LOW VOLTAGE UNDERGROUND
- COMMUNICATIONS UNDERGROUND
- EXISTING BC HYDRO POLE
- EXISTING BC HYDRO ANCHOR AND GUY WIRE

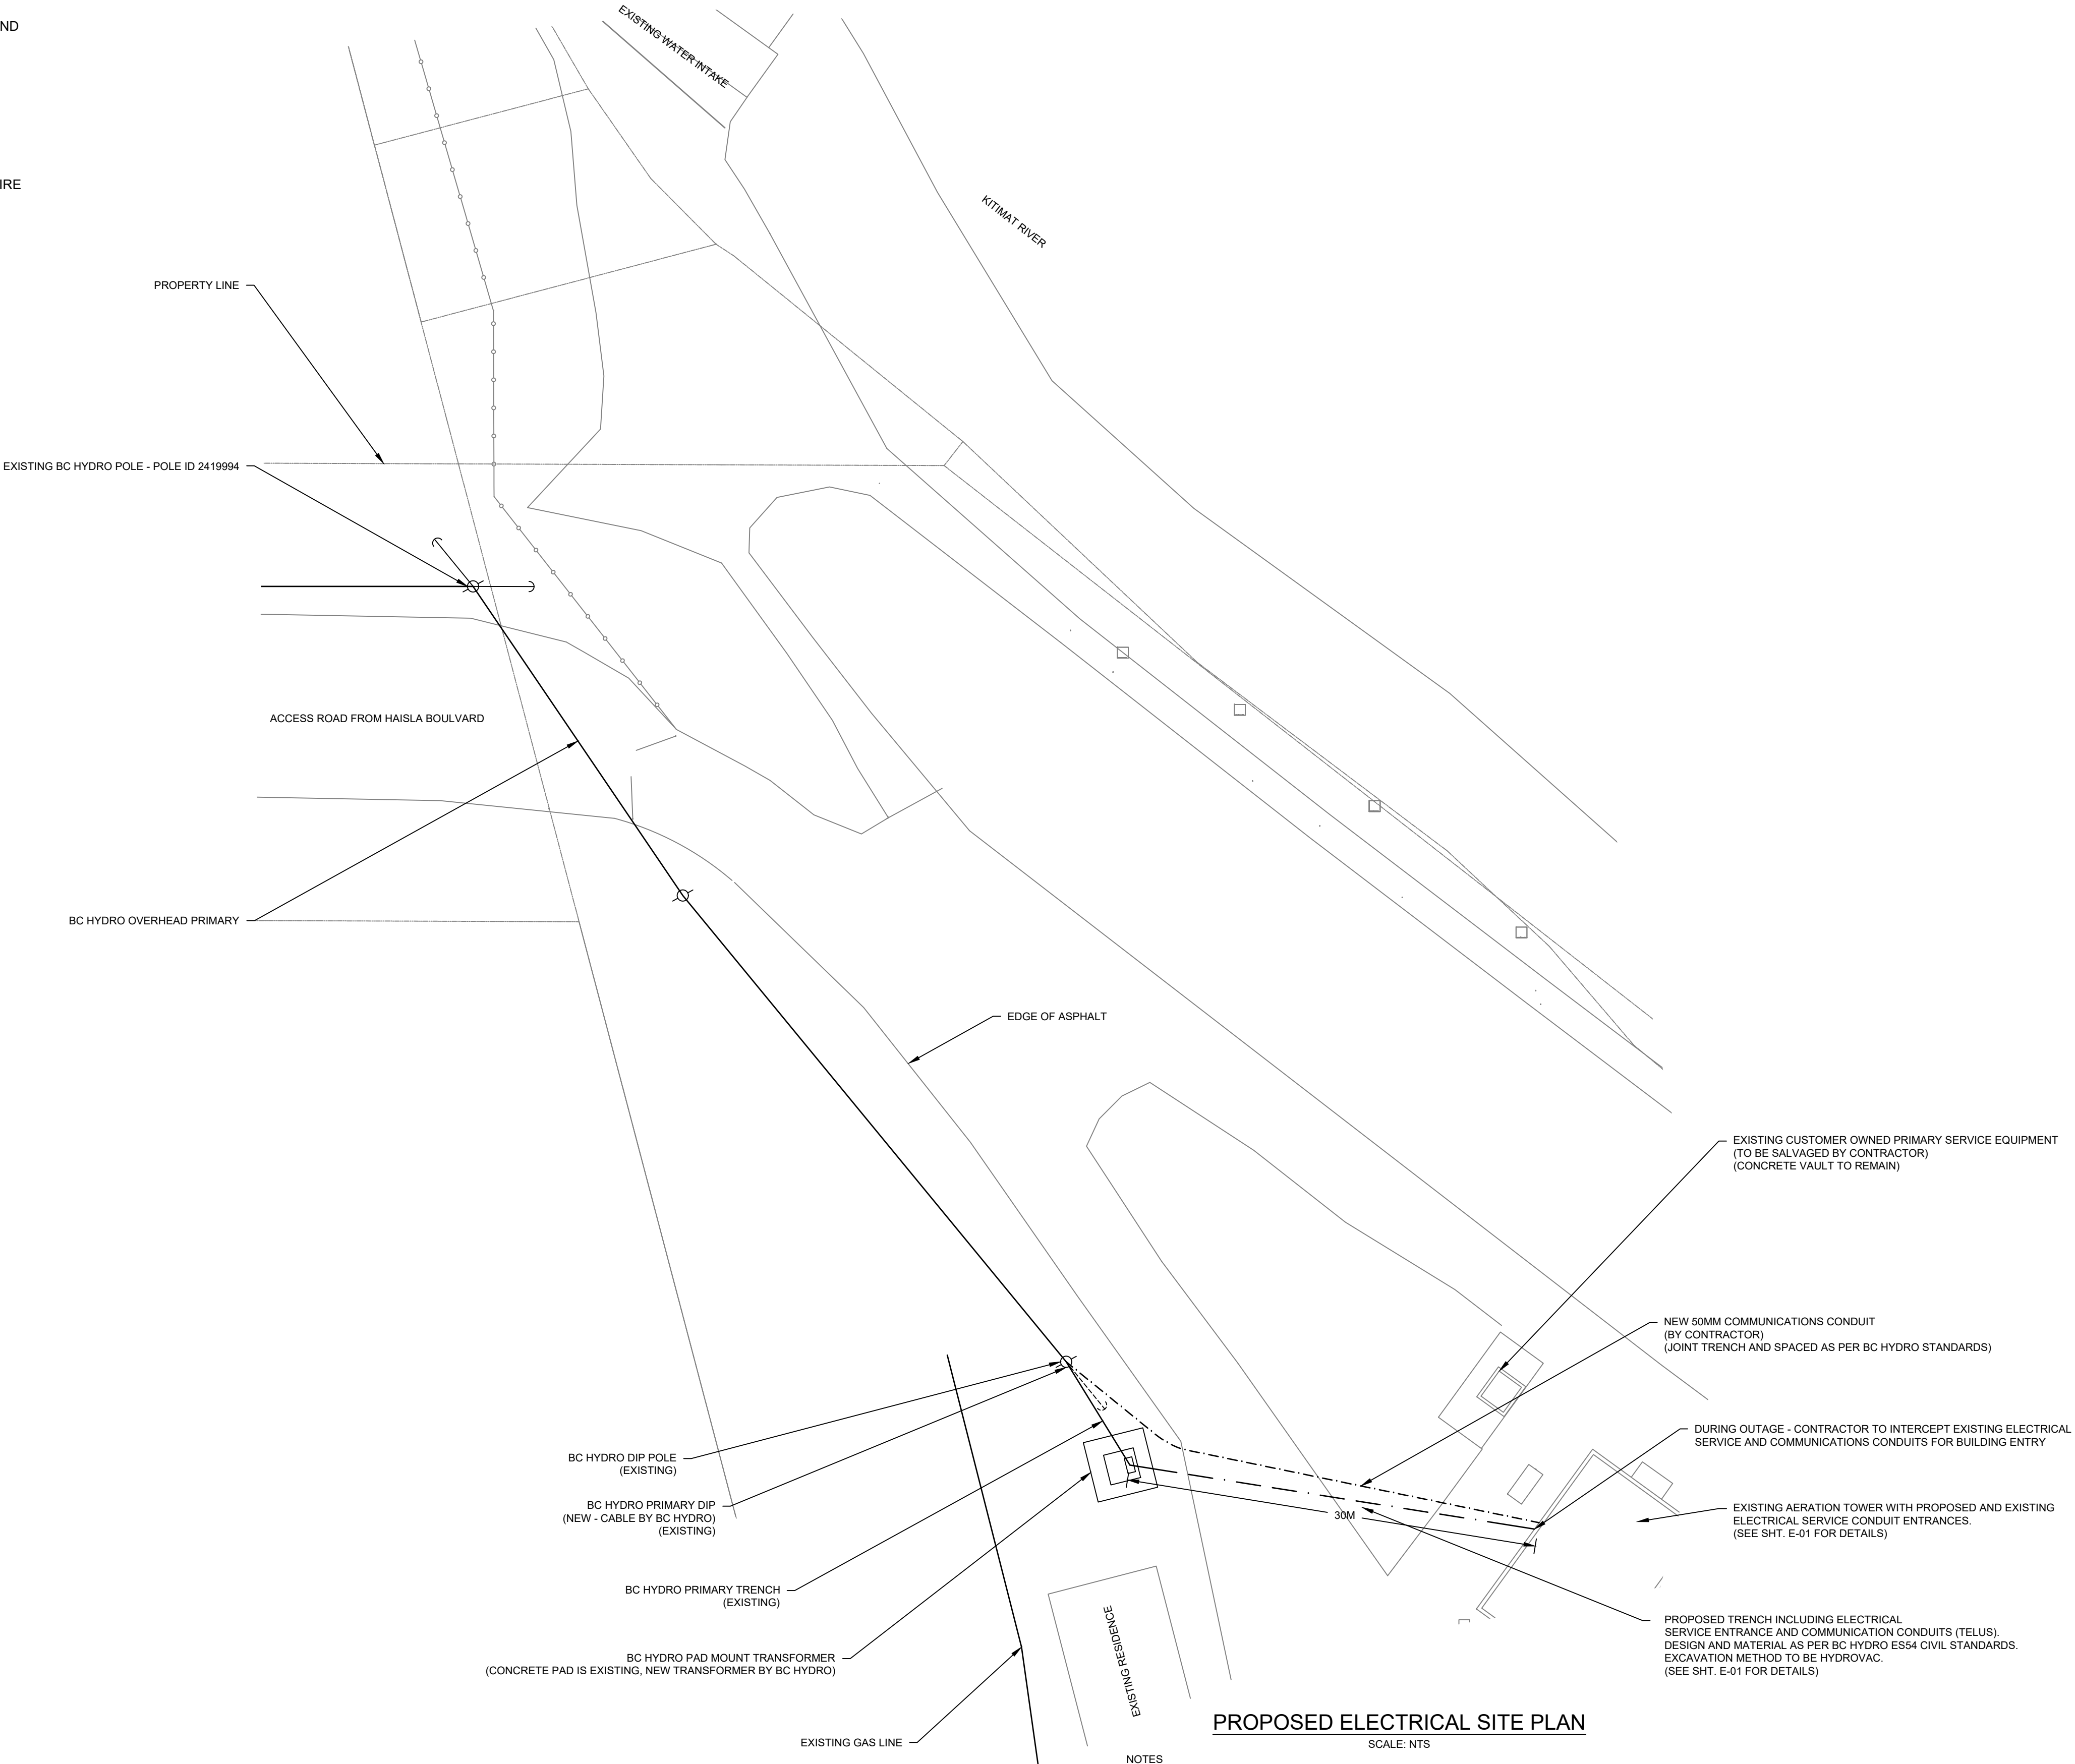

- NOTES
- ROW CLEARING FOR NEW BC HYDRO PRIMARY THREE PHASE LINE ON PRIVATE PROPERTY TO BE PROVIDED BY DEPARTMENT OF FISHERIES AND OCEANS CANADA.
 - ROW SURVEY ON PRIVATE PROPERTY TO BE COMPLETED BY DEPARTMENT OF FISHERIES AND OCEANS CANADA.
 - ALL PRIMARY AND SERVICE ENTRANCE EQUIPMENT INSTALLATION AS PER BC HYDRO STANDARDS.
 - ALL CUSTOMER EQUIPMENT TO BE INSTALLED AS PER CURRENT EDITION OF THE CANADIAN ELECTRICAL CODE.
 - CONTRACTOR TO COORDINATE INSTALLATION WITH BC HYDRO.



CONSULTING SERVICES
Terrace, BC V8G 1X6
Project No: TER-2021-006
PERMIT No: 1003300

ISSUED FOR TENDER
NOT FOR CONSTRUCTION

#	REMARKS	DATE
00	ISSUED FOR CONCEPT	27-08-2021
01	ISSUED FOR REVIEW	09-11-2021
02	RE-ISSUED FOR REVIEW AS PER BCH REQUEST	30-11-2021
03	ISSUED FOR TENDER	22-02-2022
04	ISSUED FOR REVIEW - REVISED AS PER BC HYDRO REQUEST	24-03-2025
05	RE-ISSUED FOR TENDER	13-05-2025
06	RE-ISSUED FOR TENDER	27-06-2025

DISCLAIMER

COPYRIGHT RESERVED THIS PLAN AND DESIGN ARE, AND AT ALL TIMES REMAIN THE EXCLUSIVE PROPERTY OF KYSU CONSULTING SERVICES AND CANNOT BE USED OR REPRODUCED FOR ANY REASON WHATSOEVER WITHOUT THE WRITTEN CONSENT FROM KYSU CONSULTING SERVICES

KYSU CONSULTING SERVICES IS NOT RESPONSIBLE FOR THE ACCURACY OF THESE DRAWINGS, THEY ARE ISSUED FOR INFORMATION PURPOSES ONLY. EXACT DIMENSIONS AND LOCATIONS OF ALL SERVICES SHALL BE COORDINATED AND VERIFIED WITH THE CONTRACTOR

PROJECT TITLE

DEPARTMENT OF FISHERIES
AND OCEANS - ELECTRICAL
SERVICE UPGRADE

DRAWING TITLE

ELECTRICAL SITE PLAN

DRAWN BY

D. HOBSON

CHECKED BY

L. LOGAN

SCALE

NTS

PROJECT NO.

TER-2021-006

SEAL

SHEET NO.

E-00

REVISION NO.

06



Terrace, BC V8G 1X6
Project No: TER-2021-006
PERMIT No: 1003300

ISSUED FOR TENDER
NOT FOR CONSTRUCTION

#	REMARKS	DATE
00	ISSUED FOR CONCEPT	27-08-2021
01	ISSUED FOR REVIEW	09-11-2021
02	RE-ISSUED FOR REVIEW AS PER BCH REQUEST	30-11-2021
03	ISSUED FOR TENDER	22-02-2022
04	ISSUED FOR REVIEW - REVISED AS PER BC HYDRO REQUEST	24-03-2025
05	RE-ISSUED FOR TENDER	13-05-2025
06	RE-ISSUED FOR TENDER	27-06-2025

DISCLAIMER

COPYRIGHT RESERVED THIS PLAN AND DESIGN ARE, AND AT ALL TIMES REMAIN THE EXCLUSIVE PROPERTY OF KYSU CONSULTING SERVICES AND CANNOT BE USED OR REPRODUCED FOR ANY REASON WHATSOEVER WITHOUT THE WRITTEN CONSENT FROM KYSU CONSULTING SERVICES

KYSU CONSULTING SERVICES IS NOT RESPONSIBLE FOR THE ACCURACY OF THESE DRAWINGS, THEY ARE ISSUED FOR INFORMATION PURPOSES ONLY. EXACT DIMENSIONS AND LOCATIONS OF ALL SERVICES SHALL BE COORDINATED AND VERIFIED WITH THE CONTRACTOR

PROJECT TITLE

DEPARTMENT OF FISHERIES
AND OCEANS - ELECTRICAL
SERVICE UPGRADE

DRAWING TITLE

ELECTRICAL SERVICE LAYOUT


DRAWN BY D. HOBSON

CHECKED BY L. LOGAN

SCALE NTS

PROJECT NO. TER-2021-006

SEAL	SHEET NO. E-01
	REVISION NO. 06

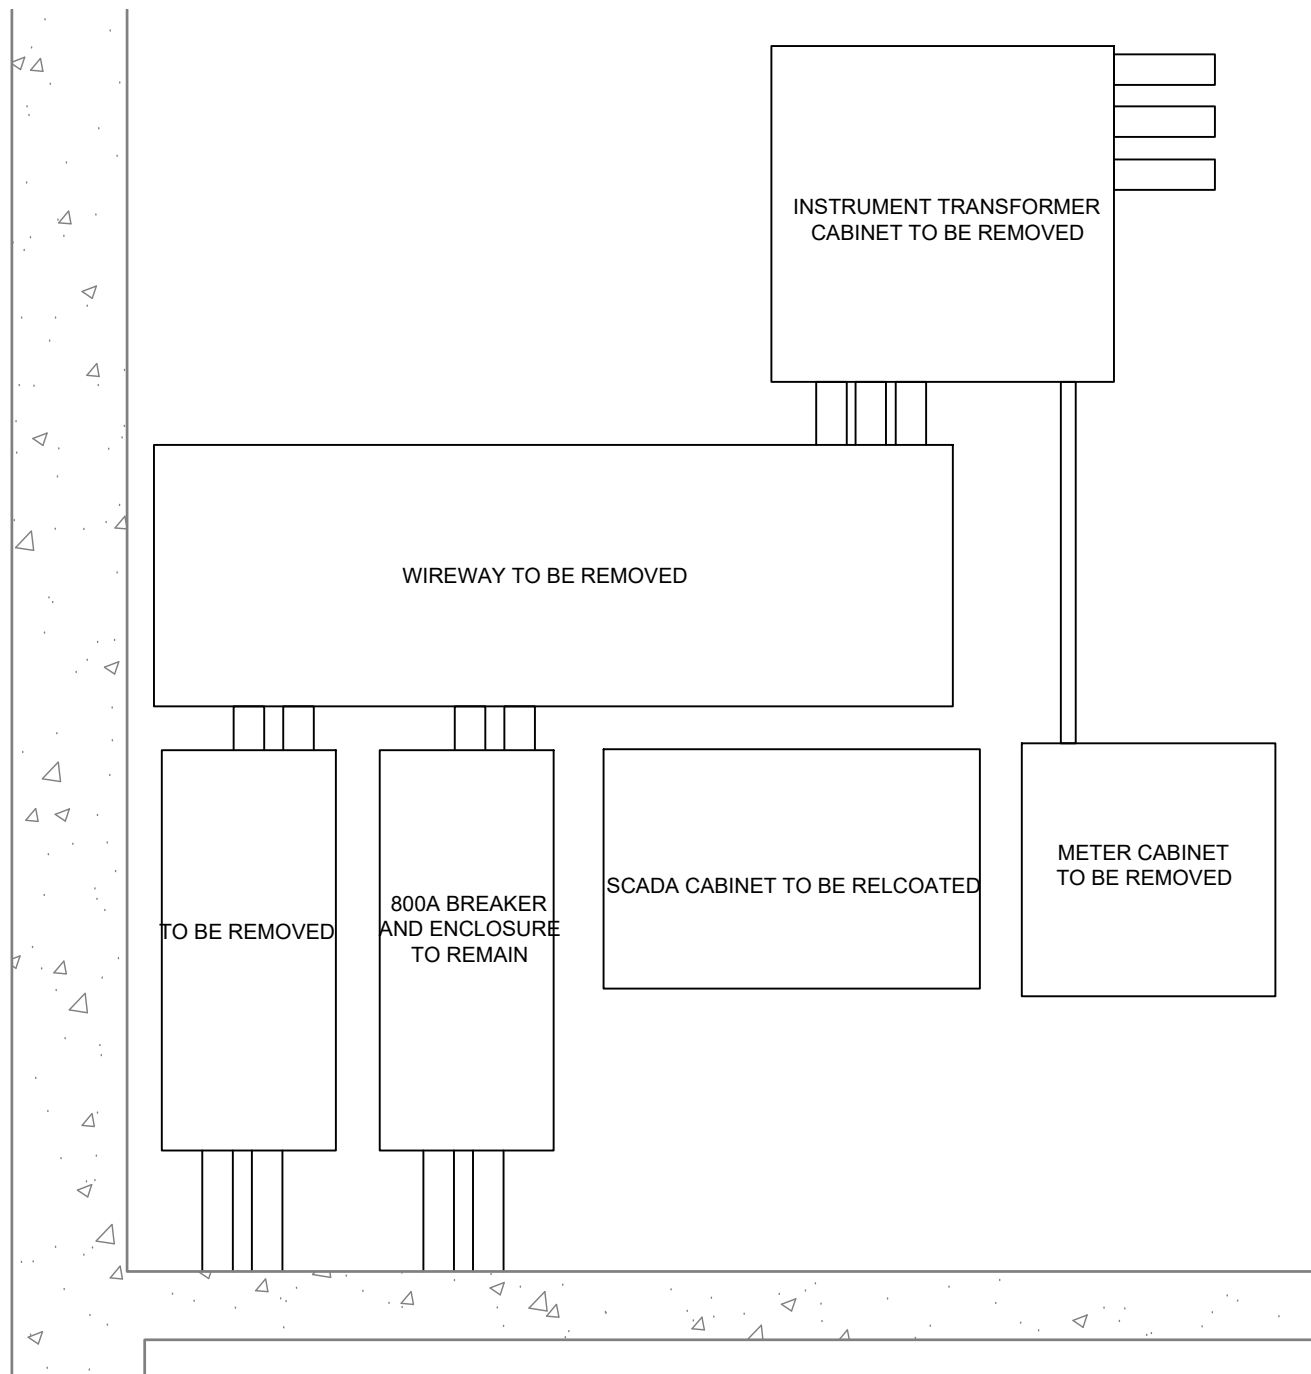


EXISTING ELECTRICAL SERVICE ENTRANCE

SCALE: 1:25

NOTES

- ALL EQUIPMENT SHOWN IS EXISTING.
- ALL CONDUITS INSTALLED ON THE WALL TO BE REMOVED AND REPLACED WITH NEW.

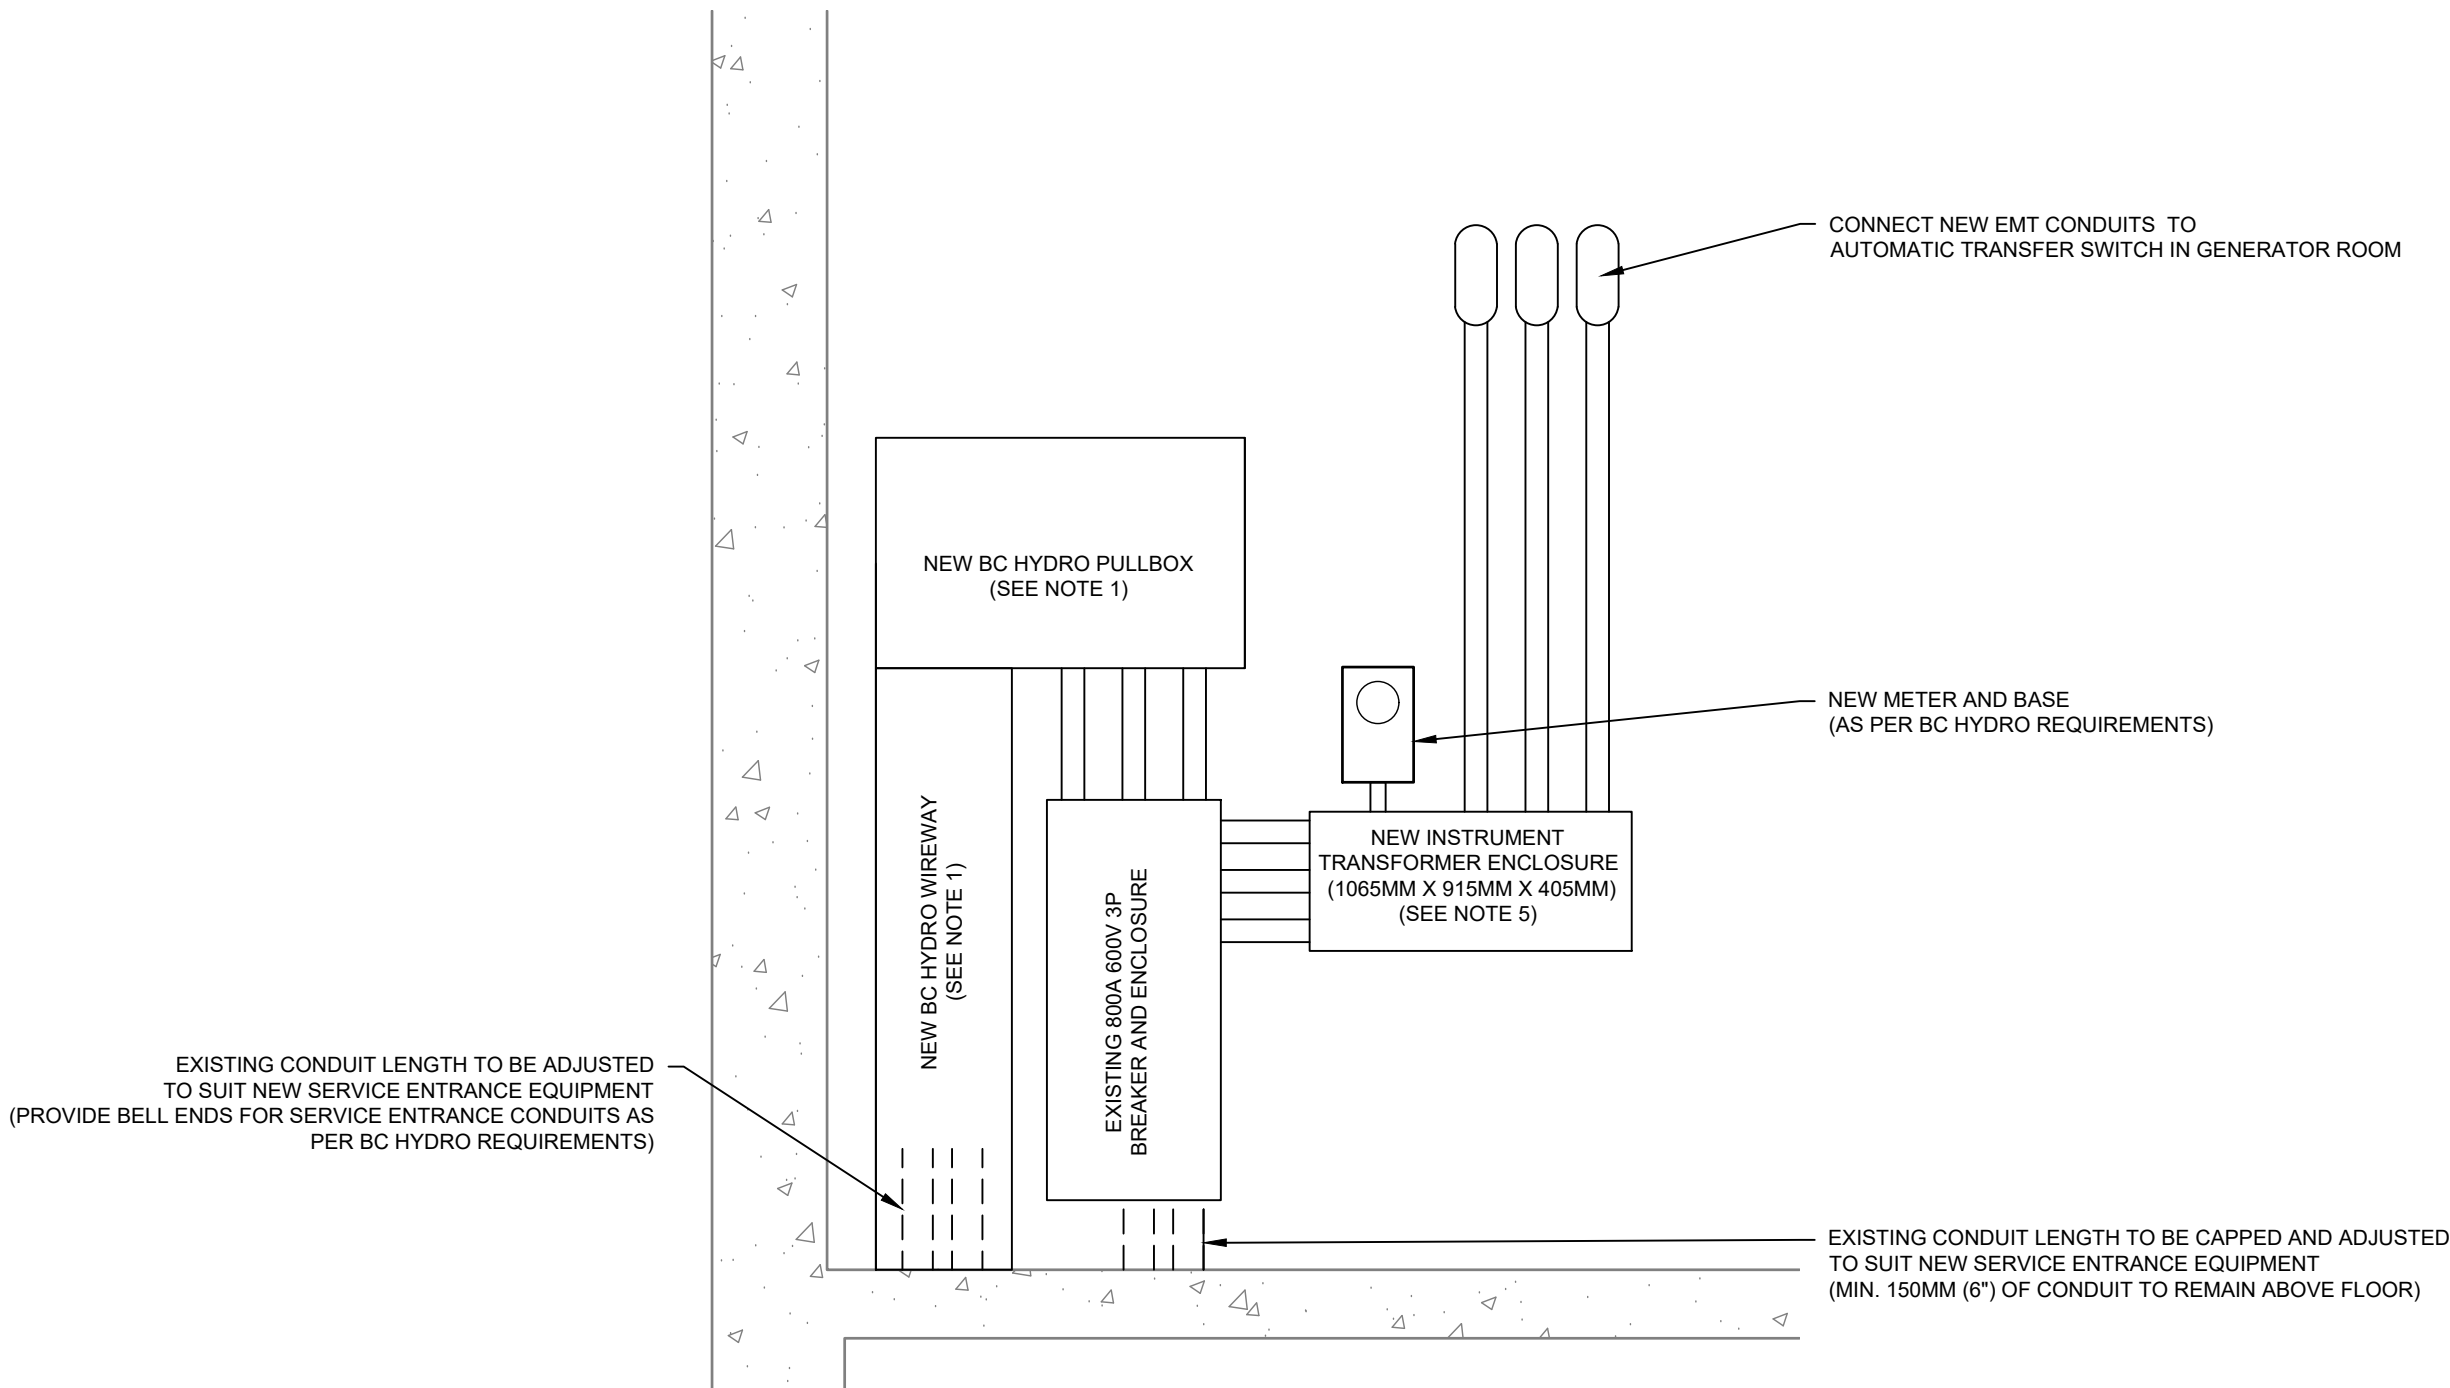


PROPOSED ELECTRICAL SERVICE ENTRANCE
SECTIONAL VIEW

SCALE: 1:25

NOTES

- ALL ELECTRICAL SERVICE EQUIPMENT TO BE PROVIDED AS PER BC HYDRO "REQUIREMENTS FOR SECONDARY VOLTAGE REVENUE METERING (750V OR LESS). SEE NOTE 5.
- ALL CUSTOMER ELECTRICAL EQUIPMENT INSTALLATION AS PER CURRENT EDITION OF THE CANADIAN ELECTRICAL CODE.
- CONFIRM EQUIPMENT LOCATION WITH OWNER PRIOR TO INSTALLATION.
- PROVIDE SHOP DRAWINGS OF ALL ELECTRICAL EQUIPMENT TO ENGINEER FOR REVIEW PRIOR TO PURCHASE.
- BC HYDRO HAS APPROVED A UNIQUE CT/PT CABINET TO ACCOMMODATE EXISTING SITE CLEARANCES. CT/PT CABINET TO BE 1065MM (42") WIDE BY 915MM (36") TALL AND 405MM (16") DEEP.

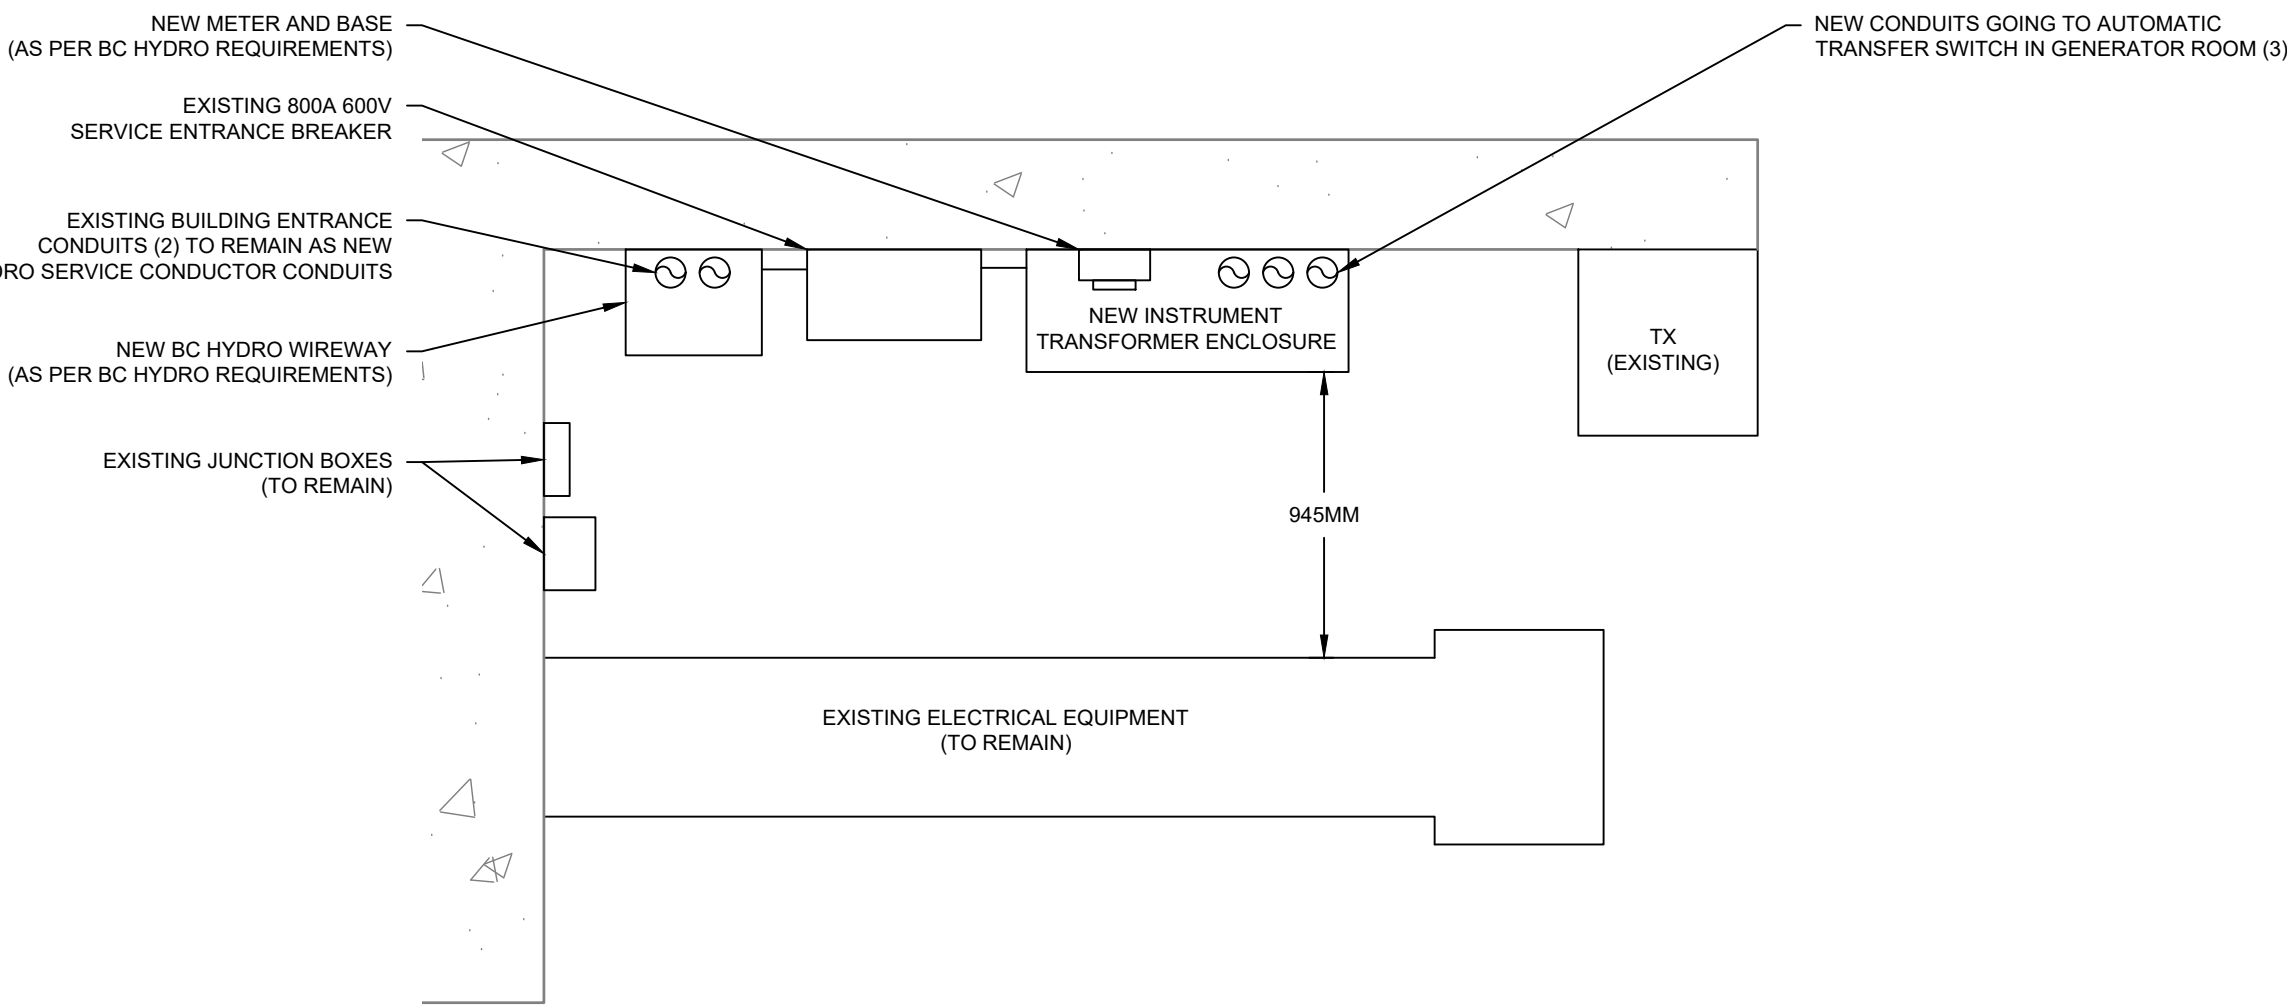



PROPOSED ELECTRICAL SERVICE ENTRANCE
- PLAN VIEW

SCALE: 1:25

NOTES

- ALL ELECTRICAL SERVICE EQUIPMENT TO BE PROVIDED AS PER BC HYDRO "REQUIREMENTS FOR SECONDARY VOLTAGE REVENUE METERING (750V OR LESS).
- ALL CUSTOMER ELECTRICAL EQUIPMENT INSTALLATION AS PER CURRENT EDITION OF THE CANADIAN ELECTRICAL CODE.
- CONFIRM EQUIPMENT LOCATION WITH OWNER PRIOR TO INSTALLATION.
- PROVIDE SHOP DRAWINGS OF ALL ELECTRICAL EQUIPMENT TO ENGINEER FOR REVIEW PRIOR TO PURCHASE.

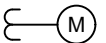SINGLE LINE SYMBOL SCHEDULE		
SYMBOL	DESCRIPTION	NOTES
	BREAKER	
	CURRENT TRANSFORMER (WITH METER) - LETTER DENOTES TYPE	
	METER - LETTER DENOTES TYPE	
	AUTOMATIC TRANSFER SWITCH	
	GENERATOR	
	GROUND	
	CONDUCTOR/FEEDER INFORMATION	

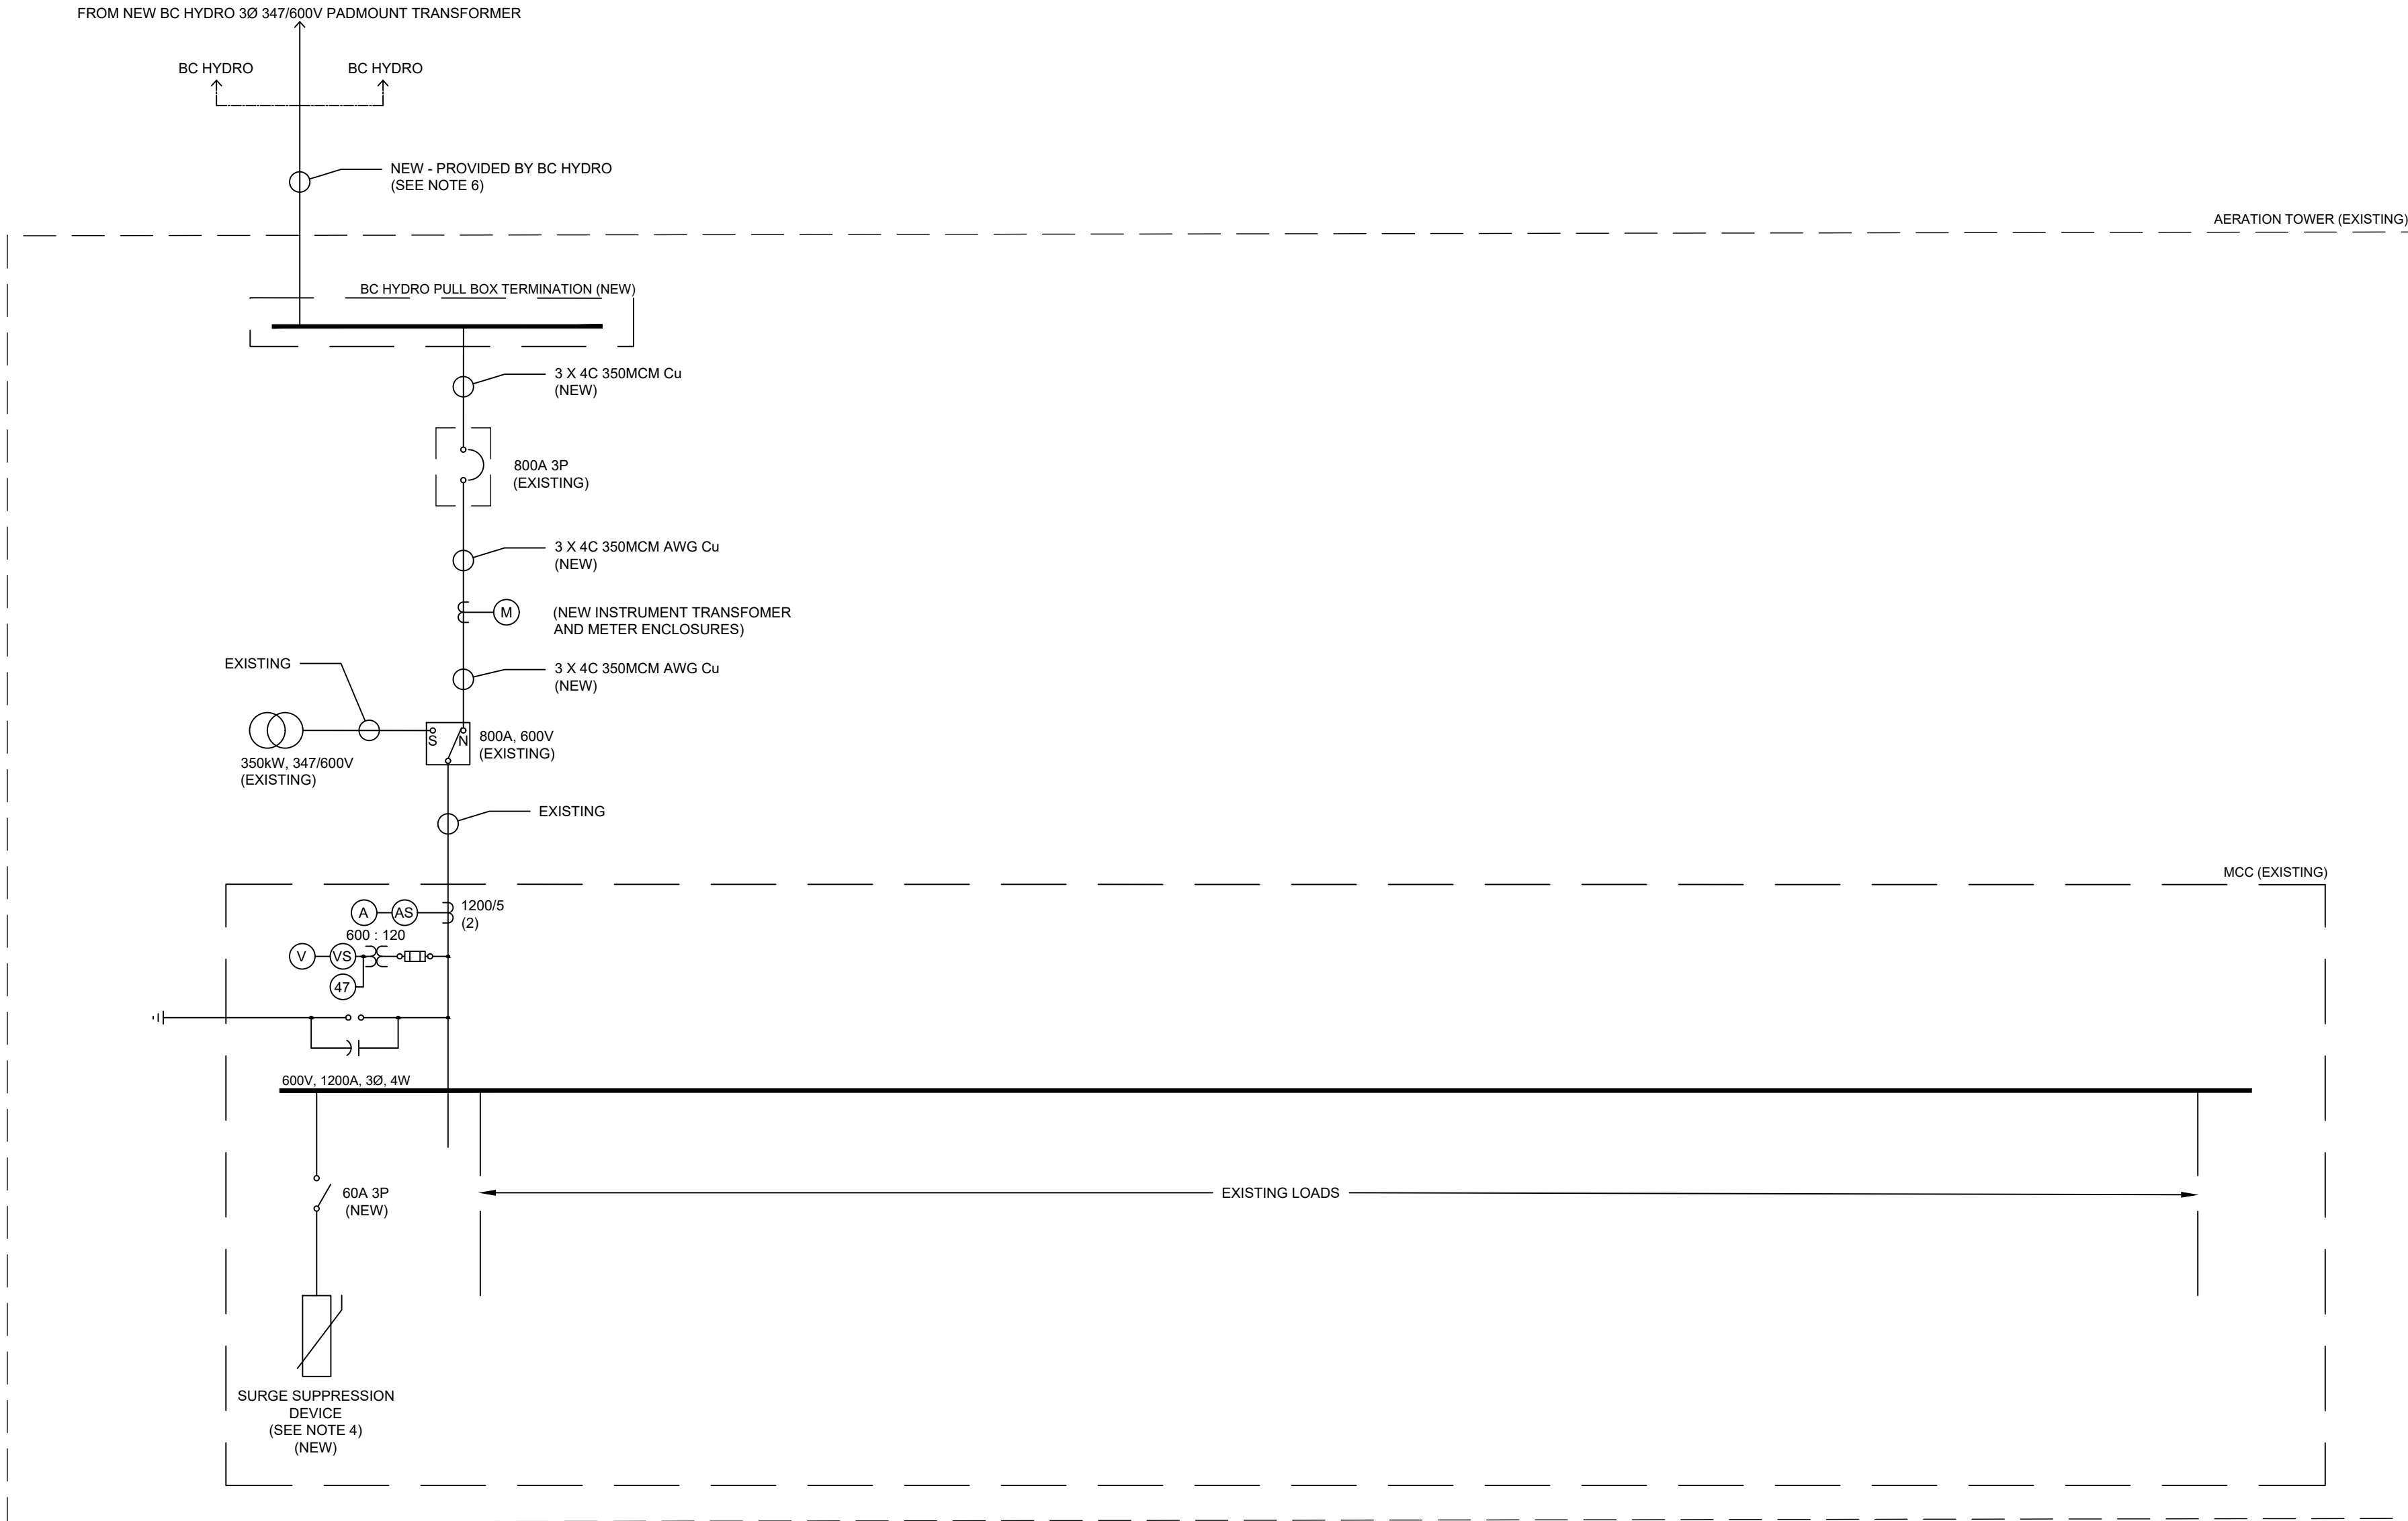

PROPOSED SINGLE LINE DIAGRAM

NOT TO SCALE

- NOTES:
- ALL INSTALLATION AS PER RECENT EDITION OF THE CEC.
 - SERVICE ENTRANCE EQUIPMENT INSTALLED AS PER BC HYDRO REQUIREMENTS.
 - CONTRACTOR TO REMOVE ALL CIVIL AND ELECTRICAL WORKS FOR EXISTING EQUIPMENT TO BE REMOVED.
 - SURGE SUPPRESSION DEVICE TO BE TOTAL PROTECTION SOLUTIONS PART# TK-ST240-3Y600 OR ENGINEER APPROVED EQUIVALENT.
 - ALL EQUIPMENT IS EXISTING UNLESS OTHERWISE NOTED.
 - CONTRACTOR TO COORDINATE INSTALLATION WITH BC HYDRO.



CONSULTING SERVICES
Terrace, BC V8G 1X6
Project No: TER-2021-006
PERMIT No: 1003300

ISSUED FOR TENDER
NOT FOR CONSTRUCTION

#	REMARKS	DATE
00	ISSUED FOR CONCEPT	27-08-2021
01	ISSUED FOR REVIEW	09-11-2021
02	RE-ISSUED FOR REVIEW AS PER BCH REQUEST	30-11-2021
03	ISSUED FOR TENDER	22-02-2022
04	ISSUED FOR REVIEW - REVISED AS PER BC HYDRO REQUEST	24-03-2025
05	RE-ISSUED FOR TENDER	13-05-2025
06	RE-ISSUED FOR TENDER	27-06-2025

DISCLAIMER

COPYRIGHT RESERVED THIS PLAN AND DESIGN ARE, AND AT ALL TIMES REMAIN THE EXCLUSIVE PROPERTY OF KYSU CONSULTING SERVICES AND CANNOT BE USED OR REPRODUCED FOR ANY REASON WHATSOEVER WITHOUT THE WRITTEN CONSENT FROM KYSU CONSULTING SERVICES

KYSU CONSULTING SERVICES IS NOT RESPONSIBLE FOR THE ACCURACY OF THESE DRAWINGS, THEY ARE ISSUED FOR INFORMATION PURPOSES ONLY. EXACT DIMENSIONS AND LOCATIONS OF ALL SERVICES SHALL BE COORDINATED AND VERIFIED WITH THE CONTRACTOR

PROJECT TITLE

DEPARTMENT OF FISHERIES
AND OCEANS - ELECTRICAL
SERVICE UPGRADE

DRAWING TITLE

ELECTRICAL SINGLE
LINE DIAGRAM

DRAWN BY D. HOBSON

CHECKED BY L. LOGAN

SCALE NTS

PROJECT NO. TER-2021-006

SEAL SHEET NO.

E-02

REVISION NO.

06